REFLECTED CEILING PLAN LEGEND:

- GYPSUM BOARD CEILING
- PVC BEADBOARD PLANKING
- VENTED VINYL SOFFIT

ELECTRIC FIXTURE LEGEND:

- CEILING MOUNTED LED LIGHT FIXTURE
- WALL MOUNTED LED LIGHT FIXTURE
- ENERGY STAR RATED EXHAUST FAN
- SD — SMOKE DETECTOR
- CEILING FAN WITH LIGHT KIT
- T — THERMOSTAT
- RECESSED LED CAN FIXTURE
- PENDANT LIGHT FIXTURE
- ELECTRIC PANEL
- LED SURFACE FIXTURE
- 4 LIGHT TRACK FIXTURE
- SECURITY CAMERA

GENERAL REFLECTED CEILING PLAN NOTES:

A) REFER TO FINISH SCHEDULE FOR CEILING MATERIALS AND FINISHES


B) PAINT GYPSUM BOARD CEILING, BULKHEADS, AND EXPOSED STRUCTURE AS SCHEDULED

C) COORDINATE LOCATION OF CEILING MOUNTED LIGHT FIXTURES, EMERGENCY LIGHTING, EMERGENCY EXIT SIGNAGE, HVAC DIFFUSERS, AND CEILING MOUNTED FIXTURES AND EQUIPMENT BETWEEN TRADES. REFER TO FLOOR PLANS, HVAC DRAWINGS, ELECTRICAL DRAWINGS, AND INTERIOR DESIGNER DRAWINGS.

D) REFERENCE ELECTRICAL DRAWINGS FOR LAYOUT SCHEDULE AND SWITCHING

KEYED REFLECTED CEILING PLAN NOTES:

1. GYP BD CEILING @ 9'-0" AFF - PAINT PER FINISH SCHEDULE
2. GYP BD CEILING @ 14'-0" AFF - PAINT PER FINISH SCHEDULE
3. VAULTED GYP BD CEILING - PAINT PER FINISH SCHEDULE
4. NOT USED
5. FAUX BEAM PER DETAILS 1/A902 AND 3/A902
6. PREFINISHED FIBER CEMENT CEILING
7. VENTED SOFFIT PER SPEC
8. PENDANT LIGHT. REF ELECTRICAL AND INTERIORS
9. 22" X 36" ATTIC ACCESS PANEL
10. TALL CUPOLA ABOVE
11. EXHAUST FAN PER MECHANICAL
12. NEW DRYWALL SOFFIT PER DETAIL 7/A902
13. DECORATIVE WOOD TRUSS PER DETAILS

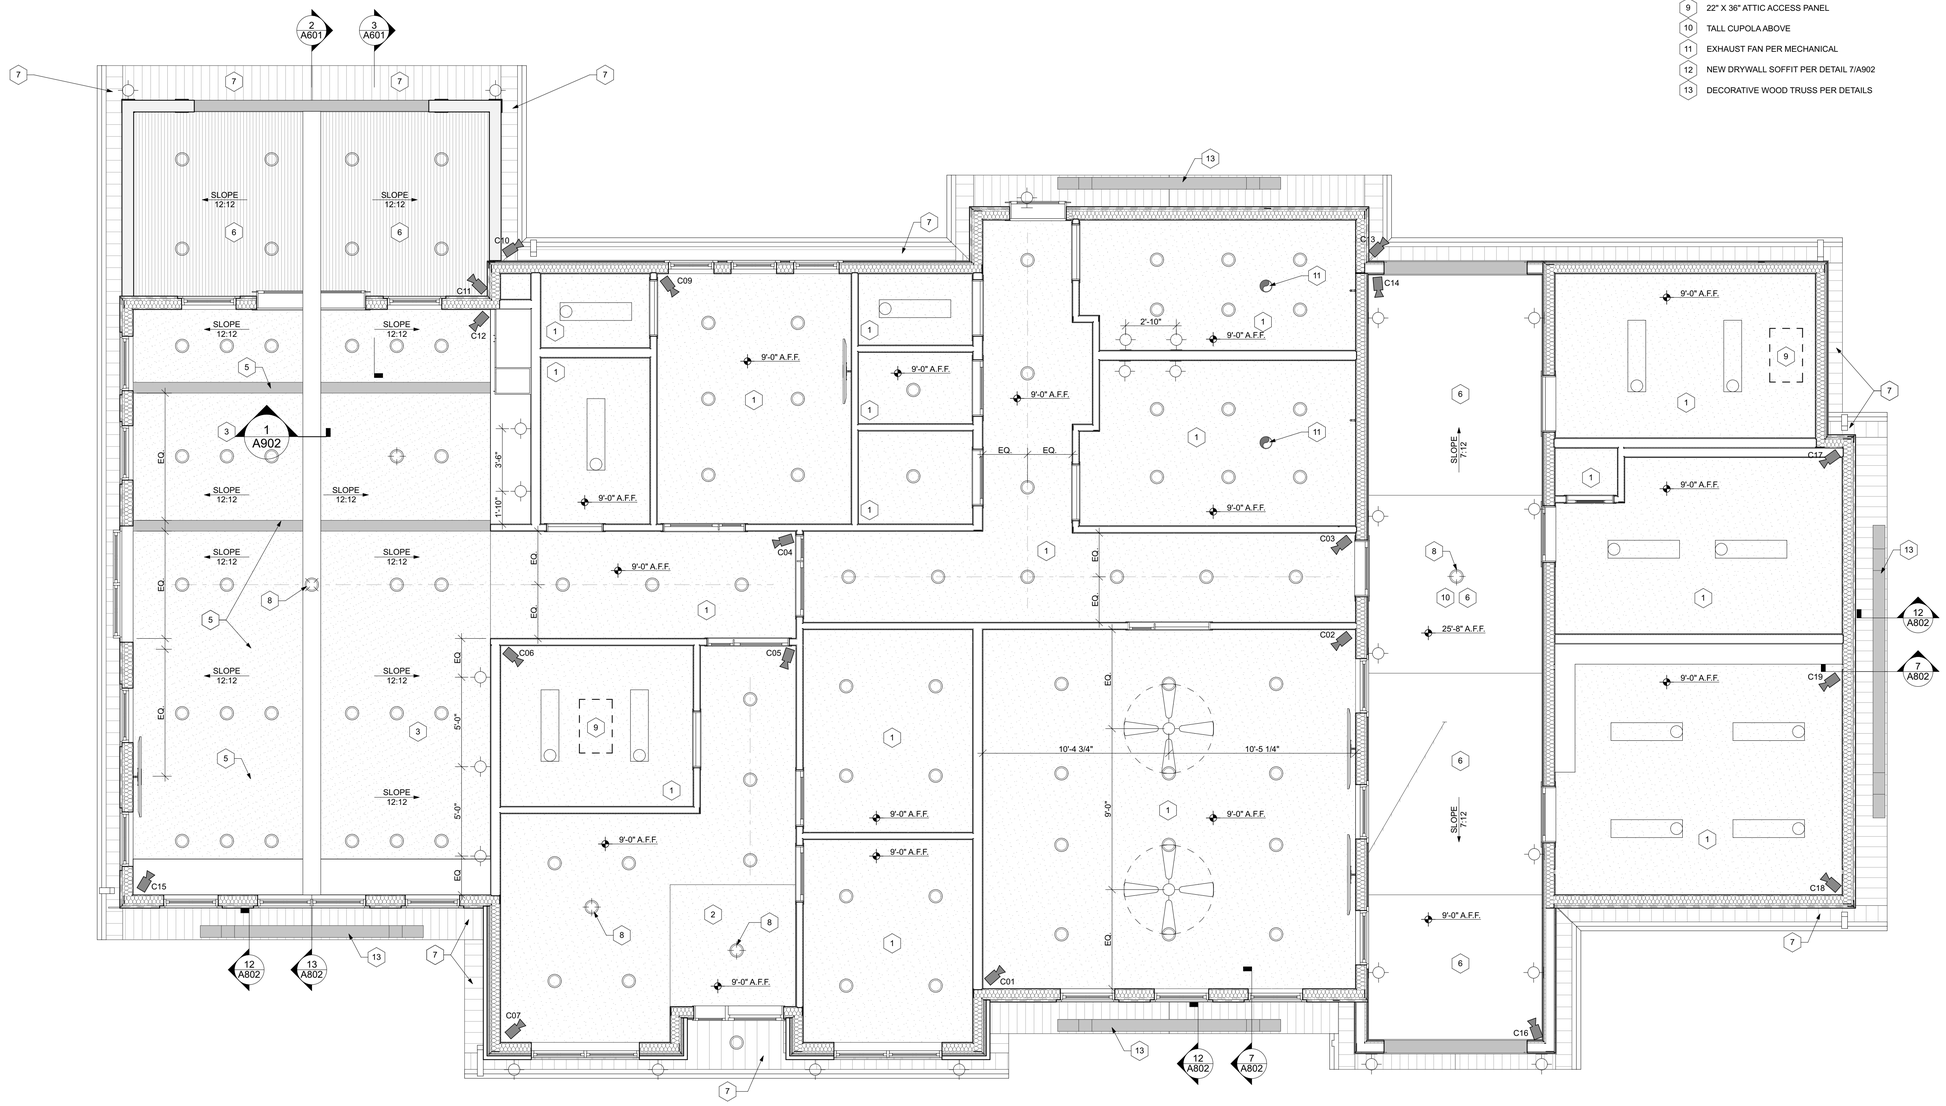

1 CLUBHOUSE REFLECTED CEILING PLAN
SCALE: 1/4" = 1'-0"

e+a
ebersoldt+associates
architecture
1214 WASHINGTON AVENUE
ST. LOUIS, MO 63103
314 + 241 4566 P
314 + 241 4939 F
WWW.EPLUSA-ARCH.COM
MO CERT OF AUTH: 2007030600

These drawings have been prepared by ebersoldt + associates architecture and contain valuable, confidential information that is the intellectual property of ebersoldt + associates architecture. Reproduction and use of these drawings without the express, written permission of ebersoldt + associates architecture is prohibited. These drawings and specifications were prepared for use on a specific project. Each project is different and the use of these drawings on projects, other than those for which they were created, may be inappropriate. ebersoldt + associates architecture assumes no responsibility or liability for the use of these documents by anyone other than the project for which they were created.
©COPYRIGHT 2024 EBERSOLDT + ASSOCIATES, LLC

STATE OF OHIO
MELISSA ANN COX
REGISTERED ARCHITECT
ARC.2218638
MELISSA COX ARC.2218638
11.11.2024

THE RESERVE AT CHATFORD
5700 CHATFORD DRIVE
COLUMBUS, OH 43232
KCG COMPANIES, LLC
9311 NORTH MERIDIAN, SUITE 100
INDIANAPOLIS, IN 46260

1" ACTUAL

IF THE ABOVE DIMENSION DOES NOT MEASURE ONE INCH (1") EXACTLY, THIS DRAWING WILL HAVE BEEN ENLARGED OR REDUCED, AFFECTING ALL LABELED SCALES.

ISSUE DESCRIPTION	DATE
OHFA APPLICATION	08.09.2024
PERMIT SET	09.20.2024
BID SET	12.17.2024

REVISIONS	
DESCRIPTION	DATE

SCALE:	AS NOTED
JOB:	23-02-007

A300
PLOTTED ON: 12/18/24

CLUBHOUSE REFLECTED CEILING PLAN